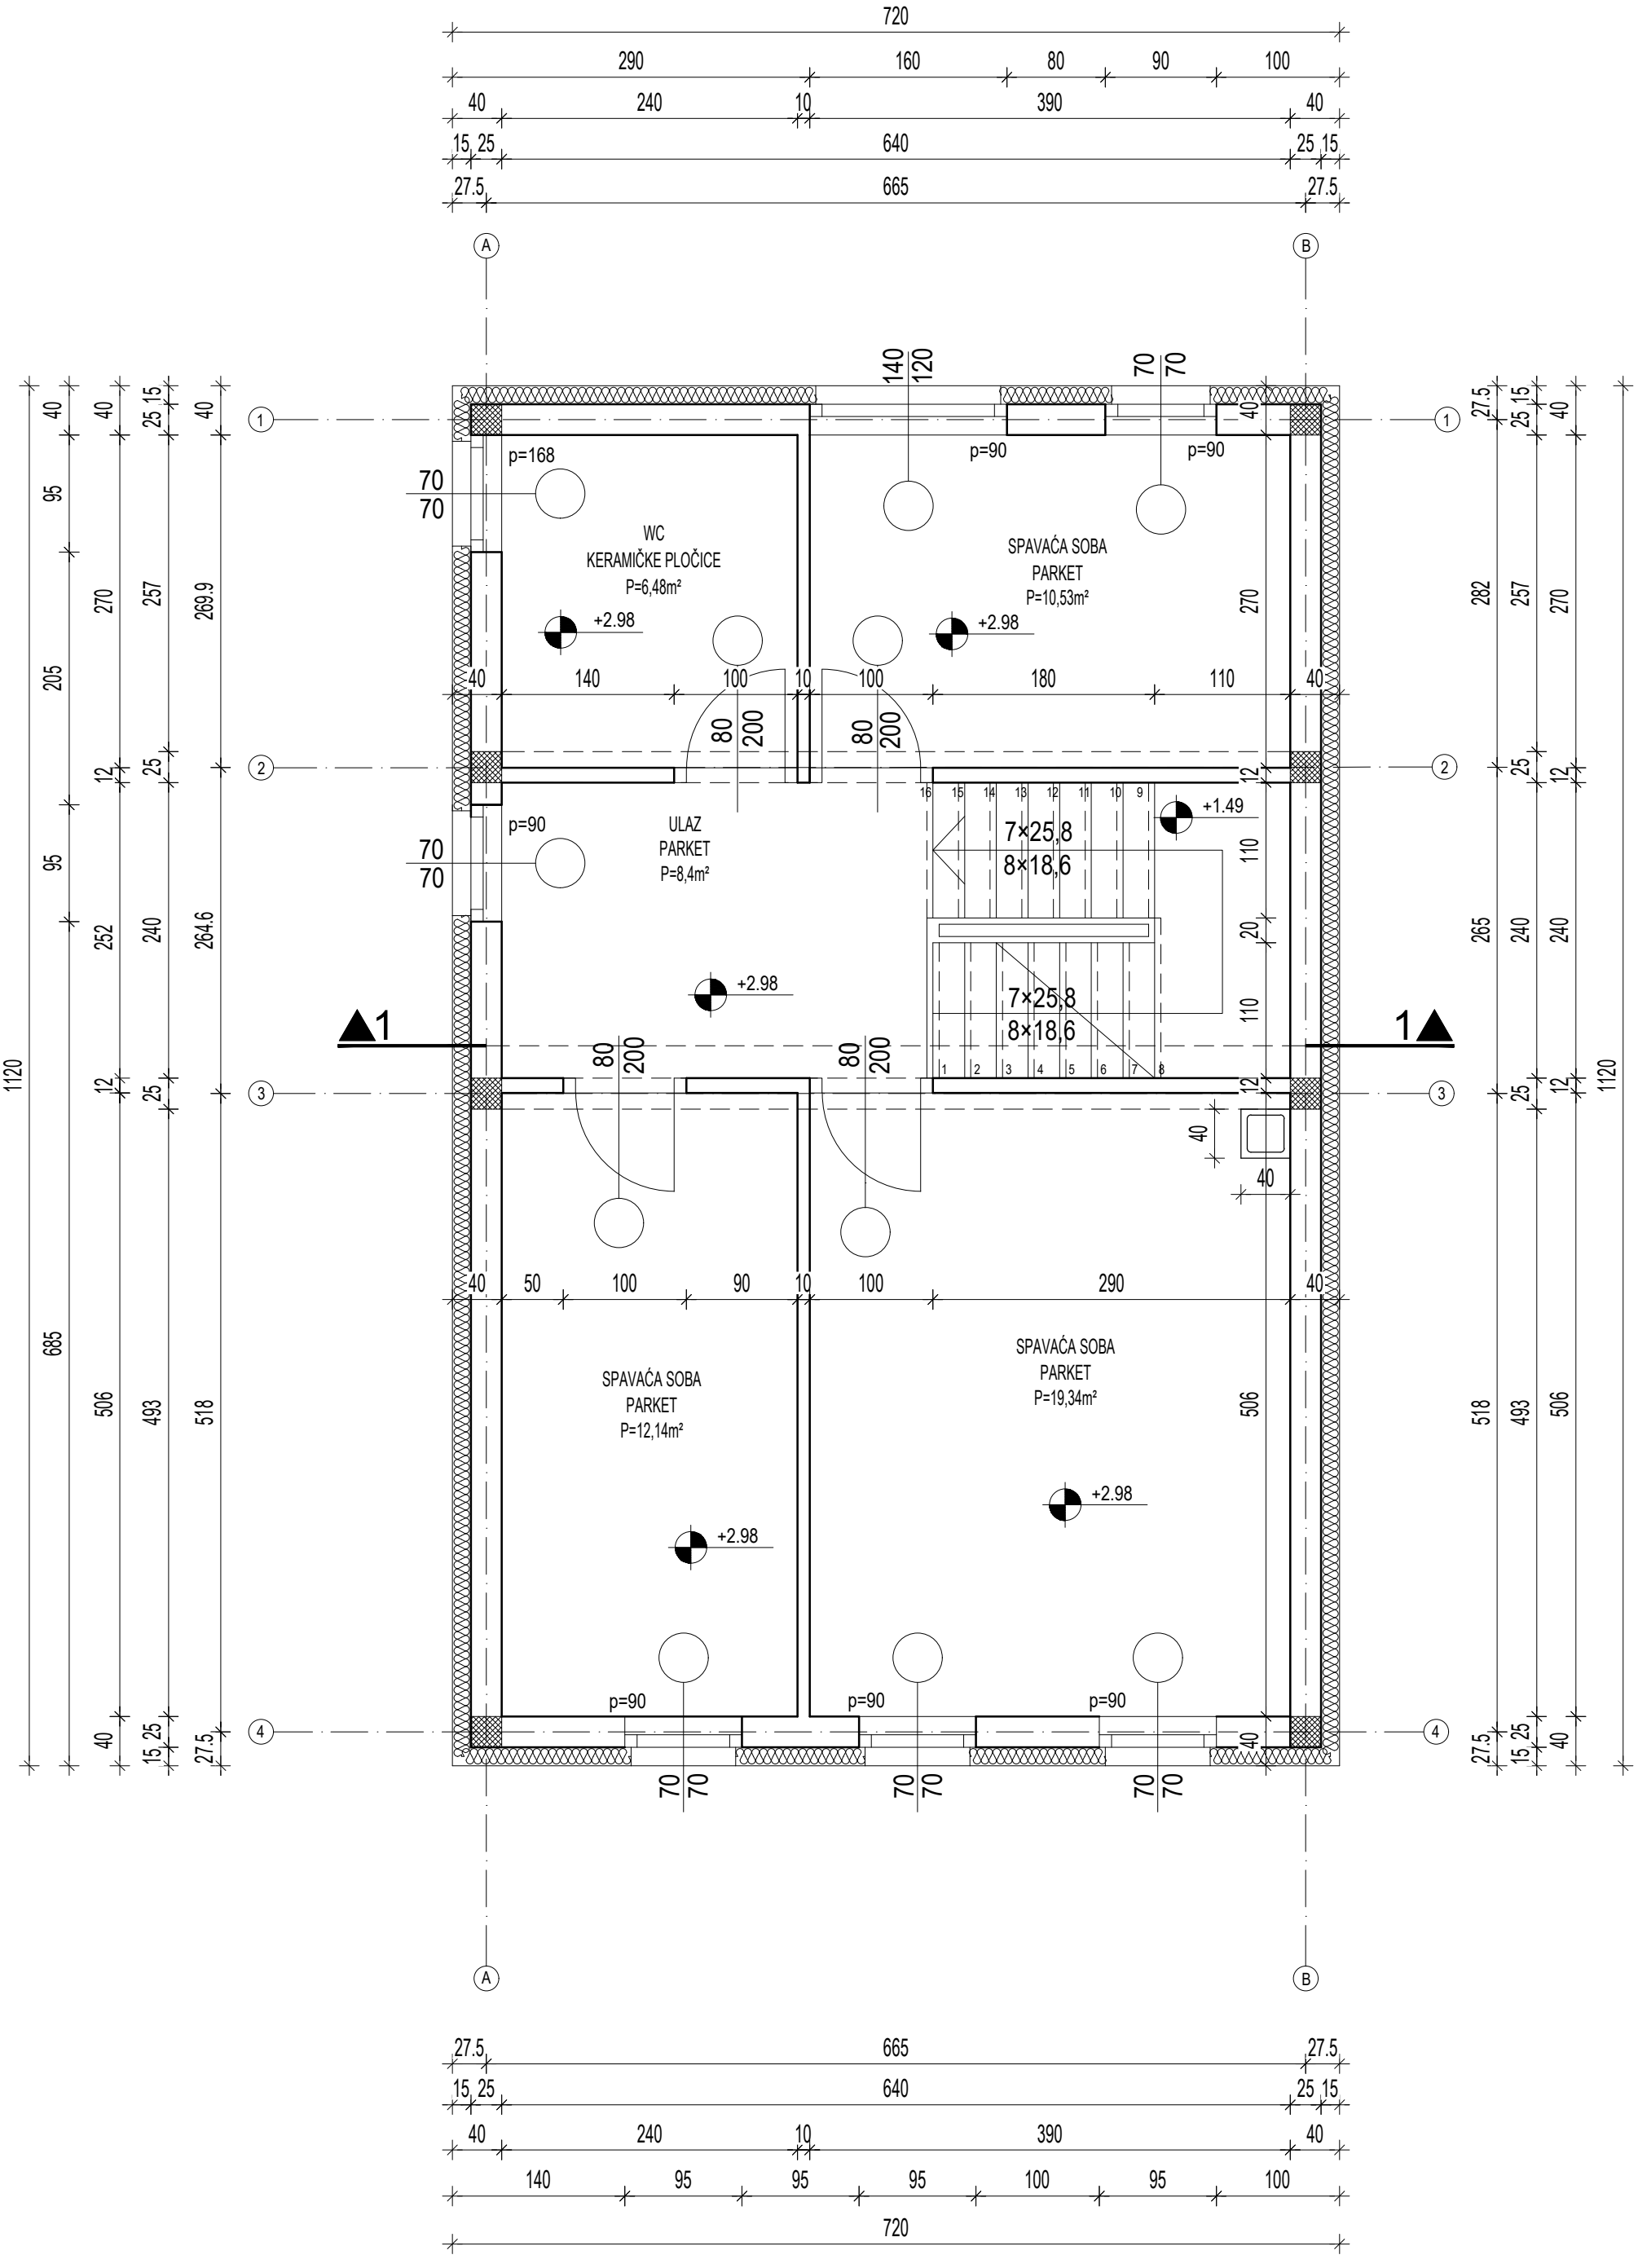


EZ	TLOCRT KATA IZVEDBENI PROJEKT ANDREA MATIJIĆ, GRUPA D	M 1:50