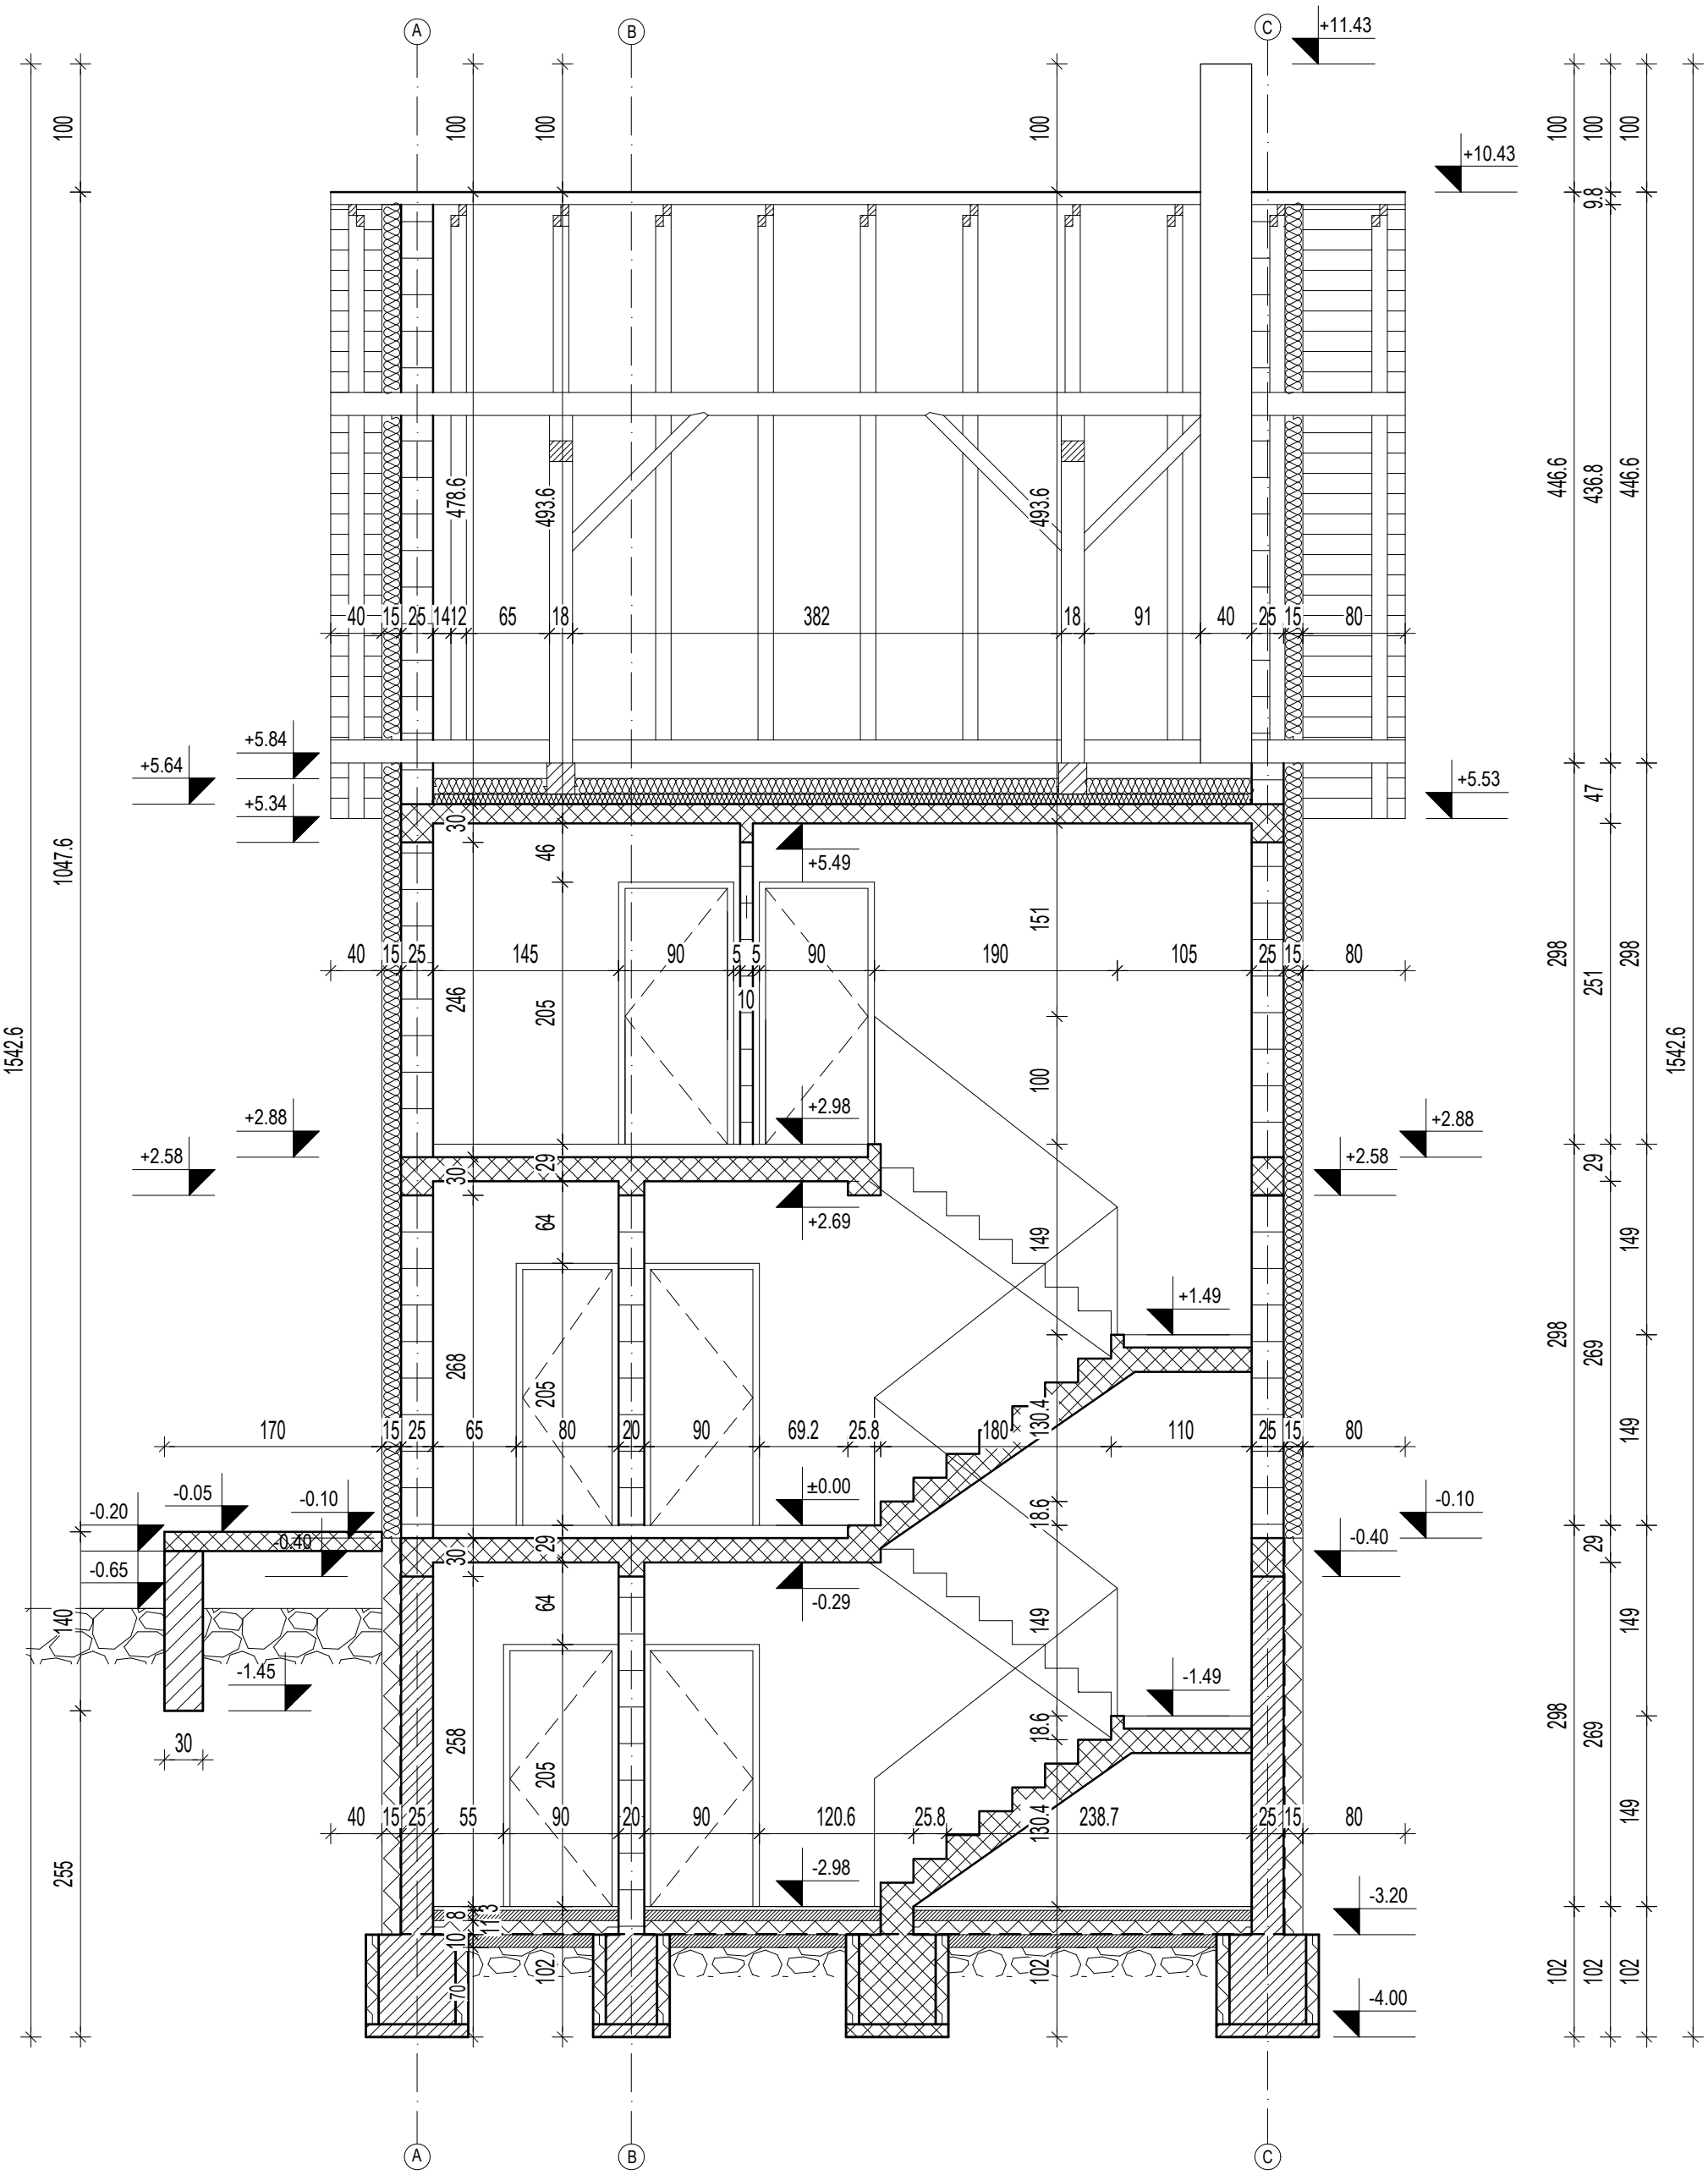


EZ	PRESJEK 1 IZVEDBENI PROJEKT	M 1:50
	ANDREA MATIJIĆ, GRUPA D	