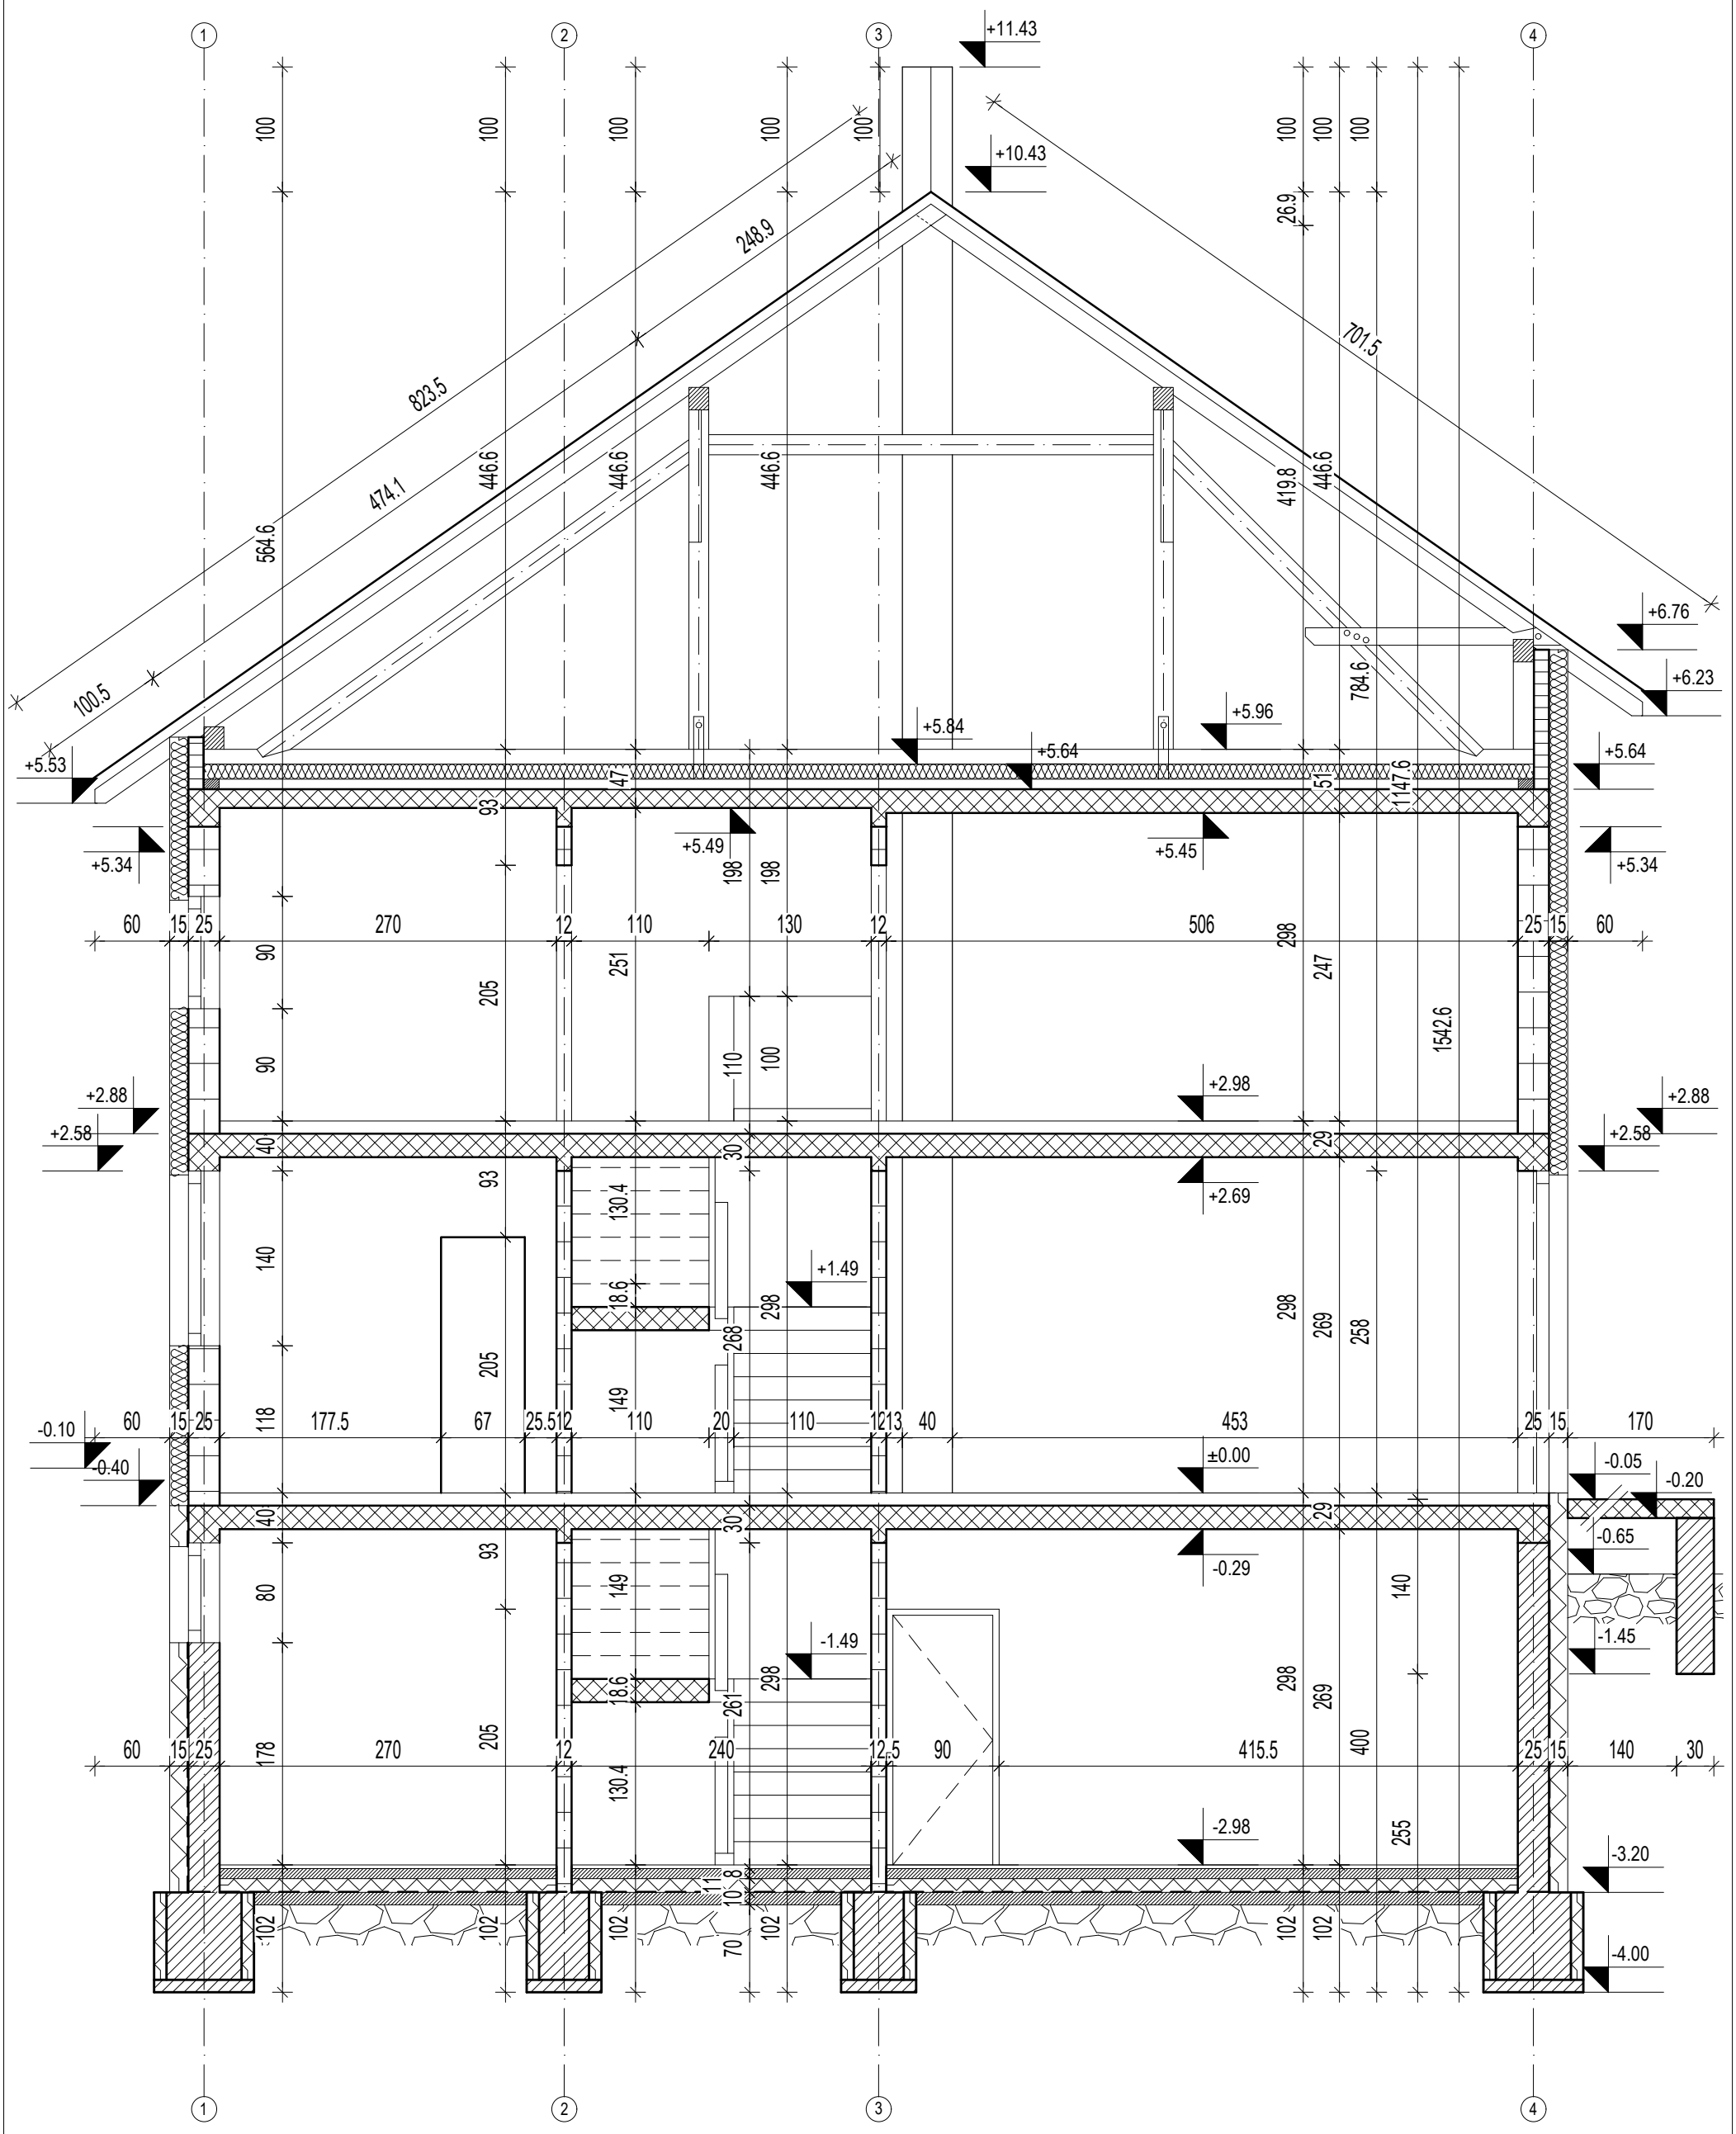


EZ	PRESJEK 2 IZVEDBENI PROJEKT ANDREA MATIJIĆ, GRUPA D	M 1:50