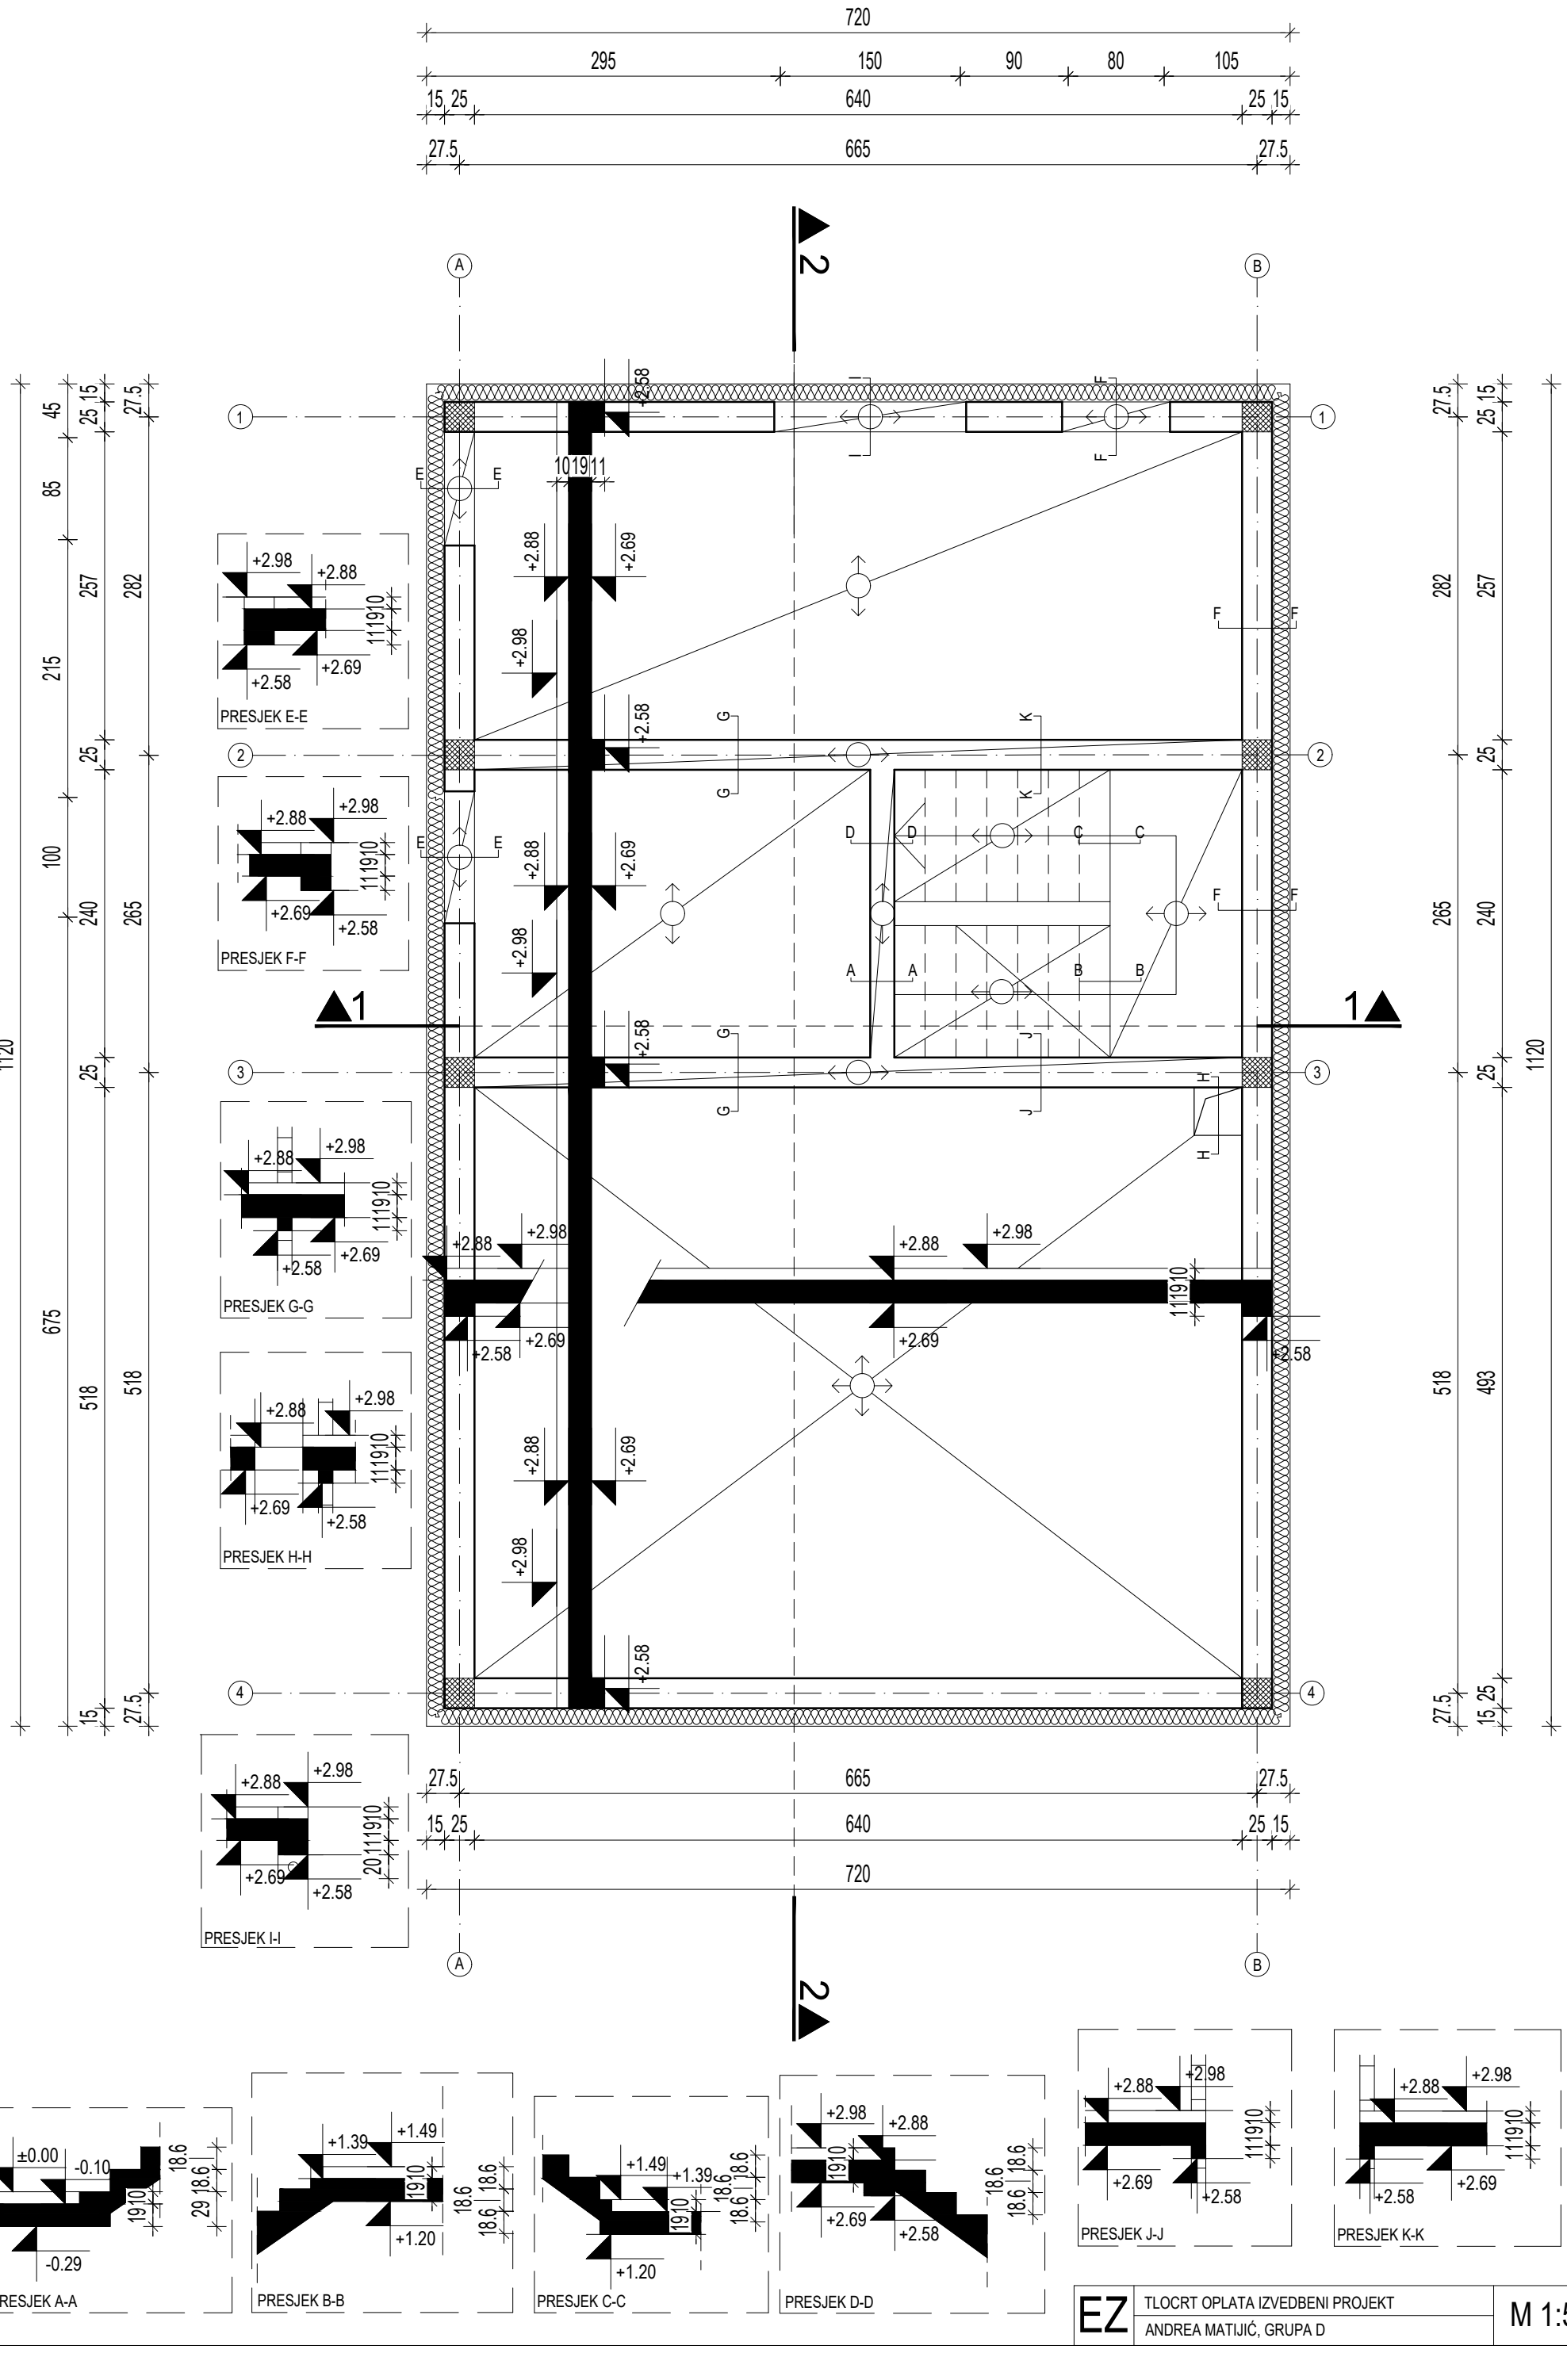


EZ | TLOCRT OPLATA IZVEDBENI PROJEKT | ANDREA MATIJIĆ, GRUPA D | M 1:50