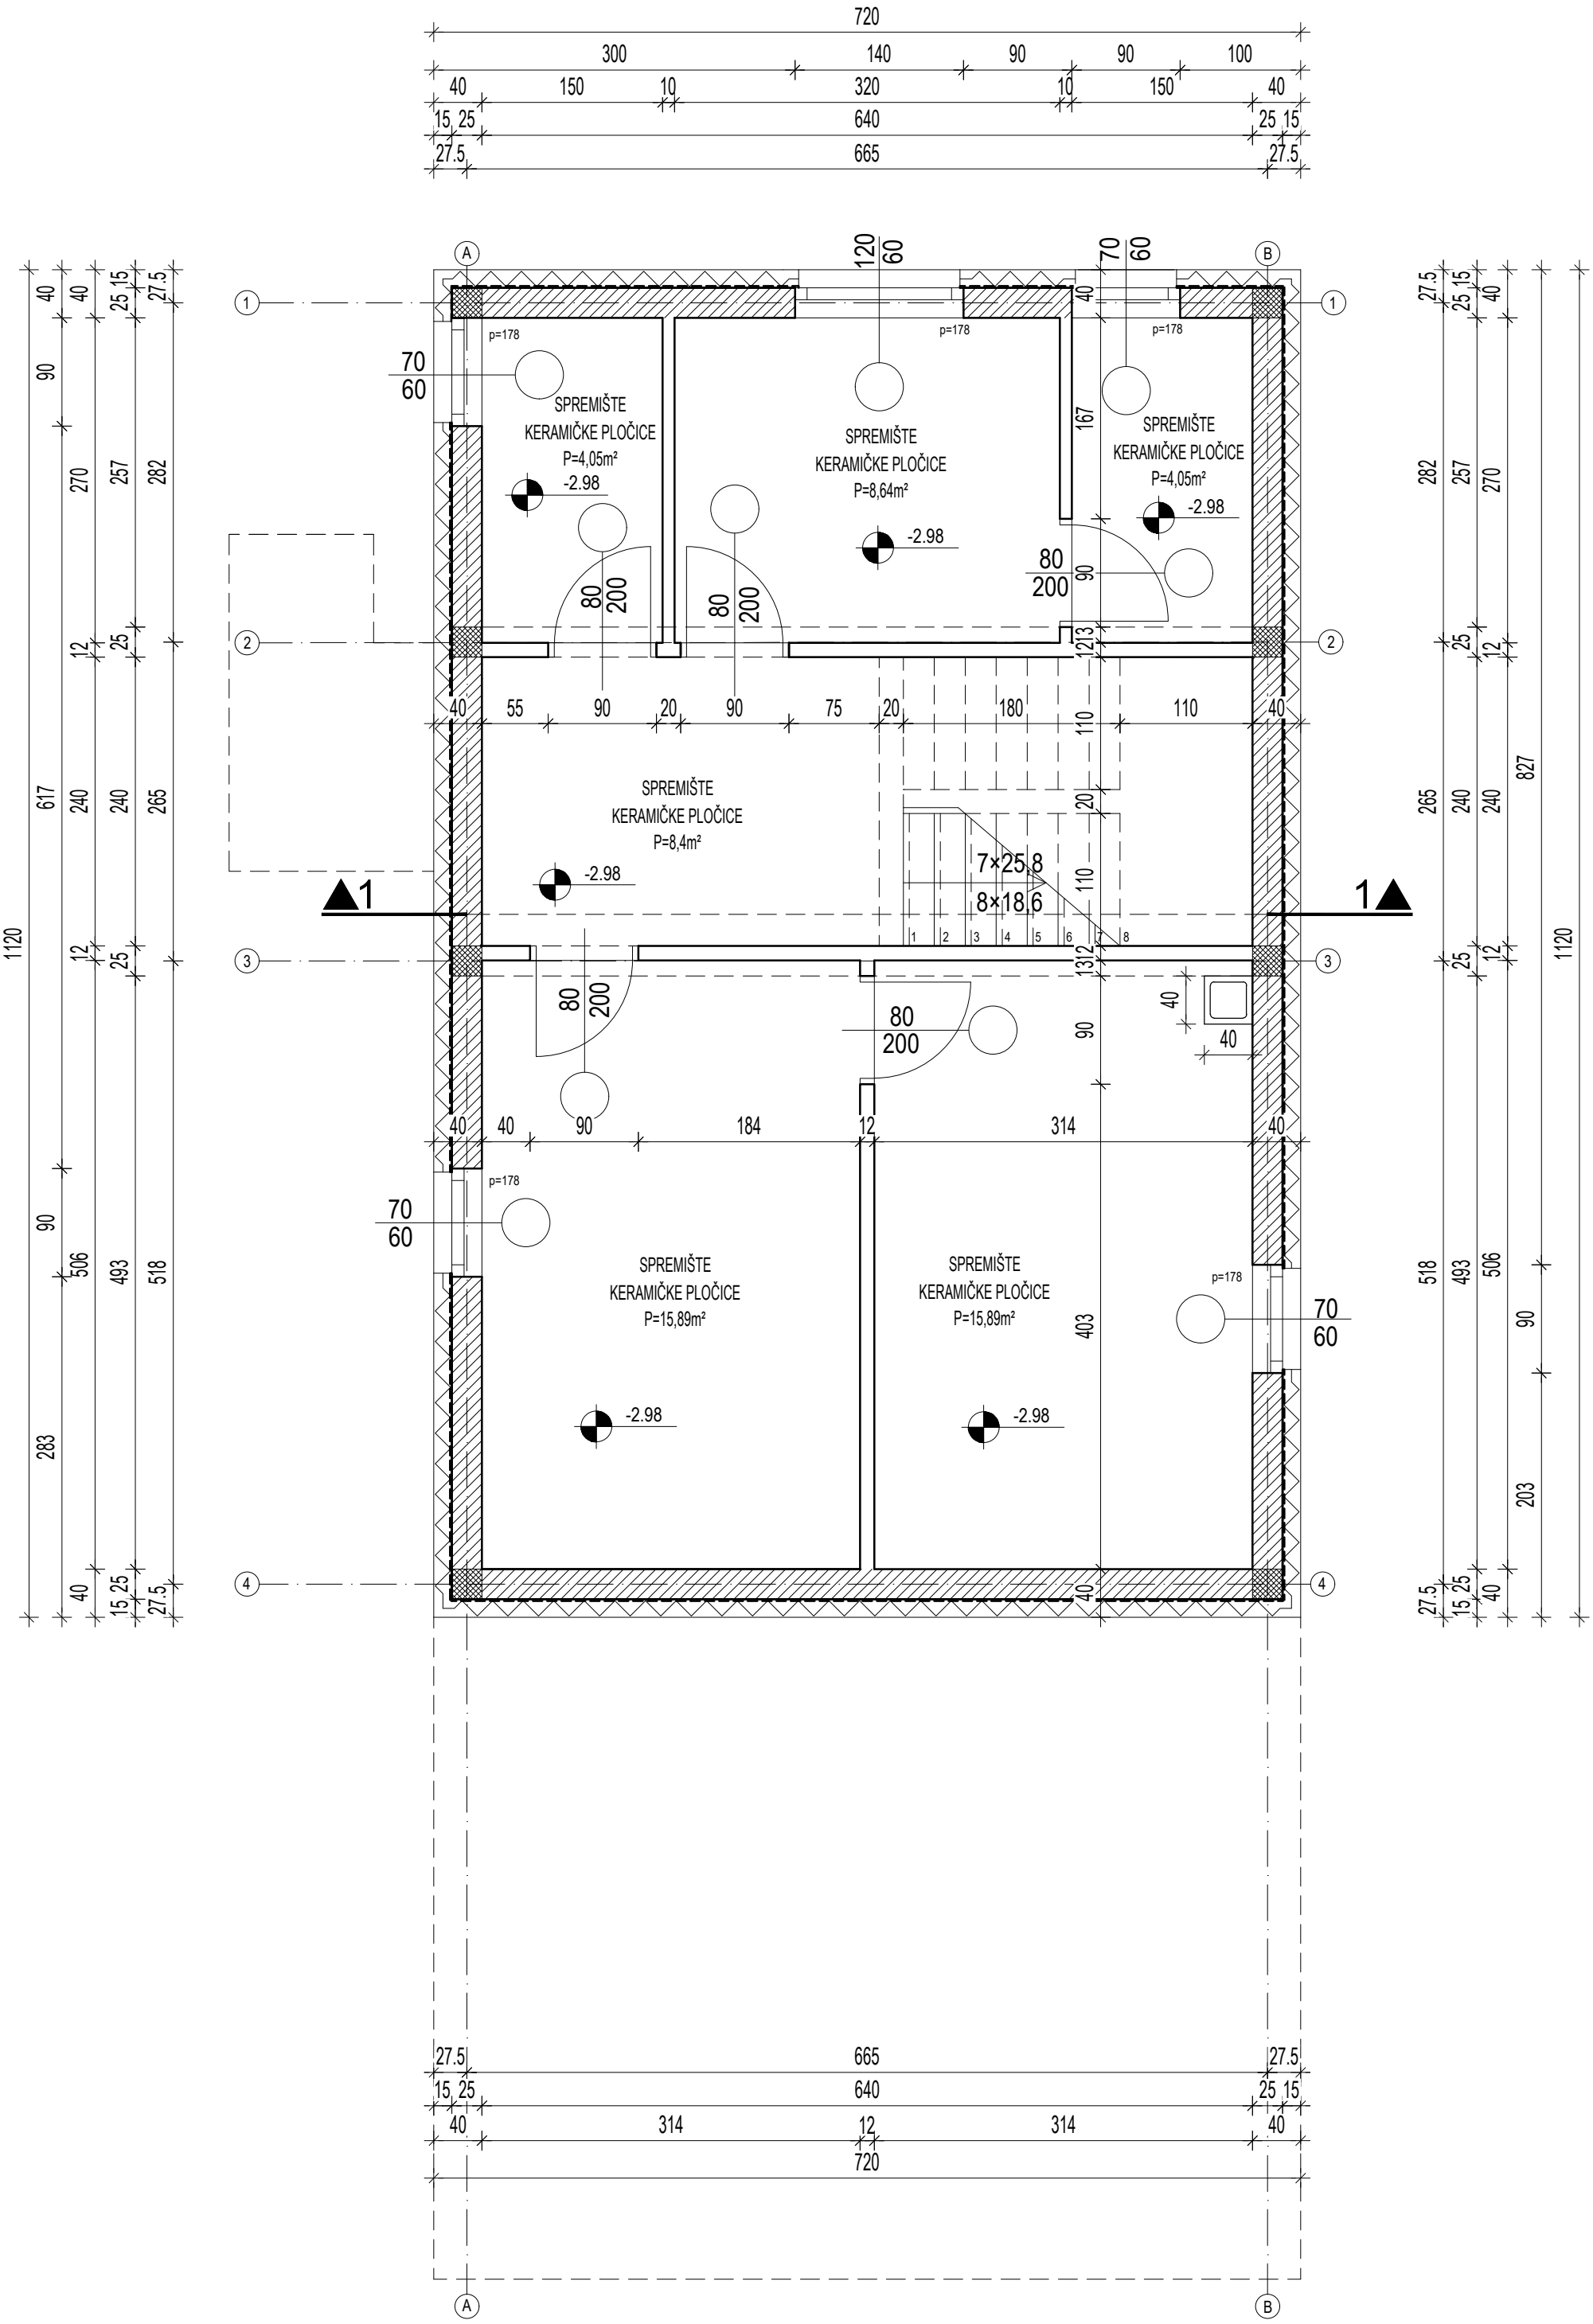



| | | |
|---|---|---|
| EZ | TLOCRT PODRUMA IZVEDBENI PROJEKT<br>ANDREA MATIJIĆ, GRUPA D | M 1:50 |