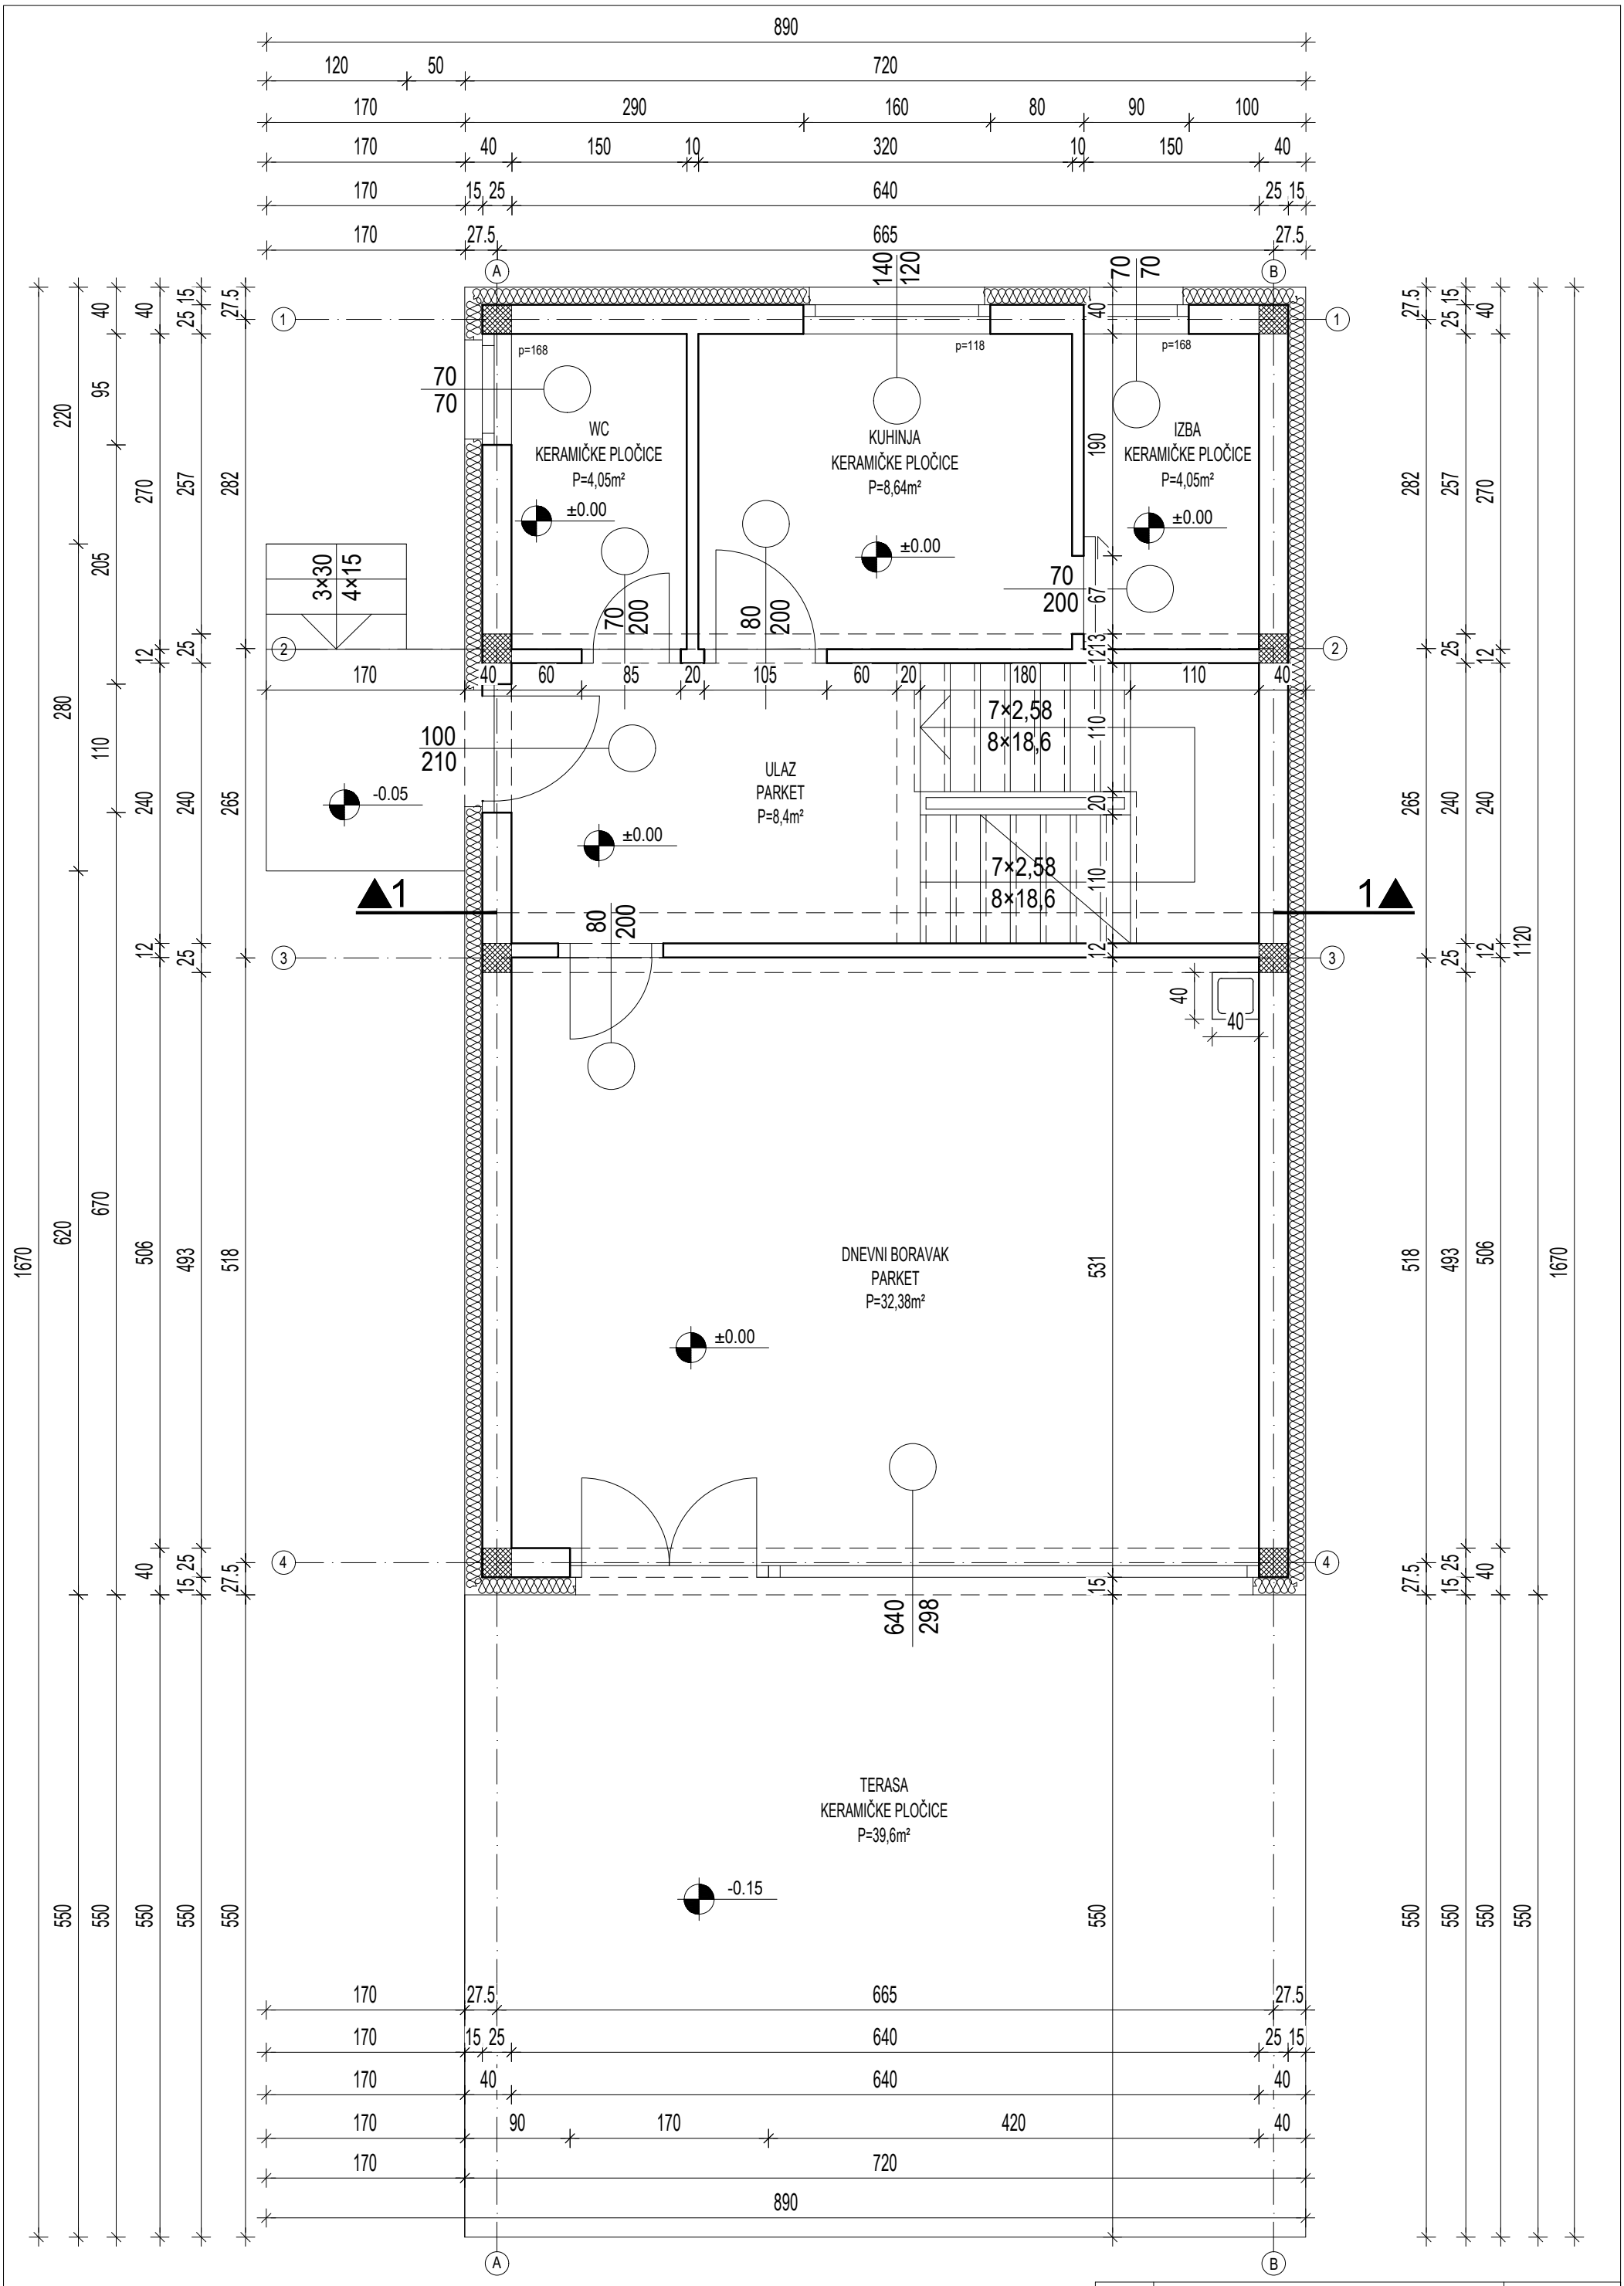


EZ	TLOCRT PRIZEMLJA IZVEDBENI PROJEKT ANDREA MATIJIĆ, GRUPA D	MJ 1:50